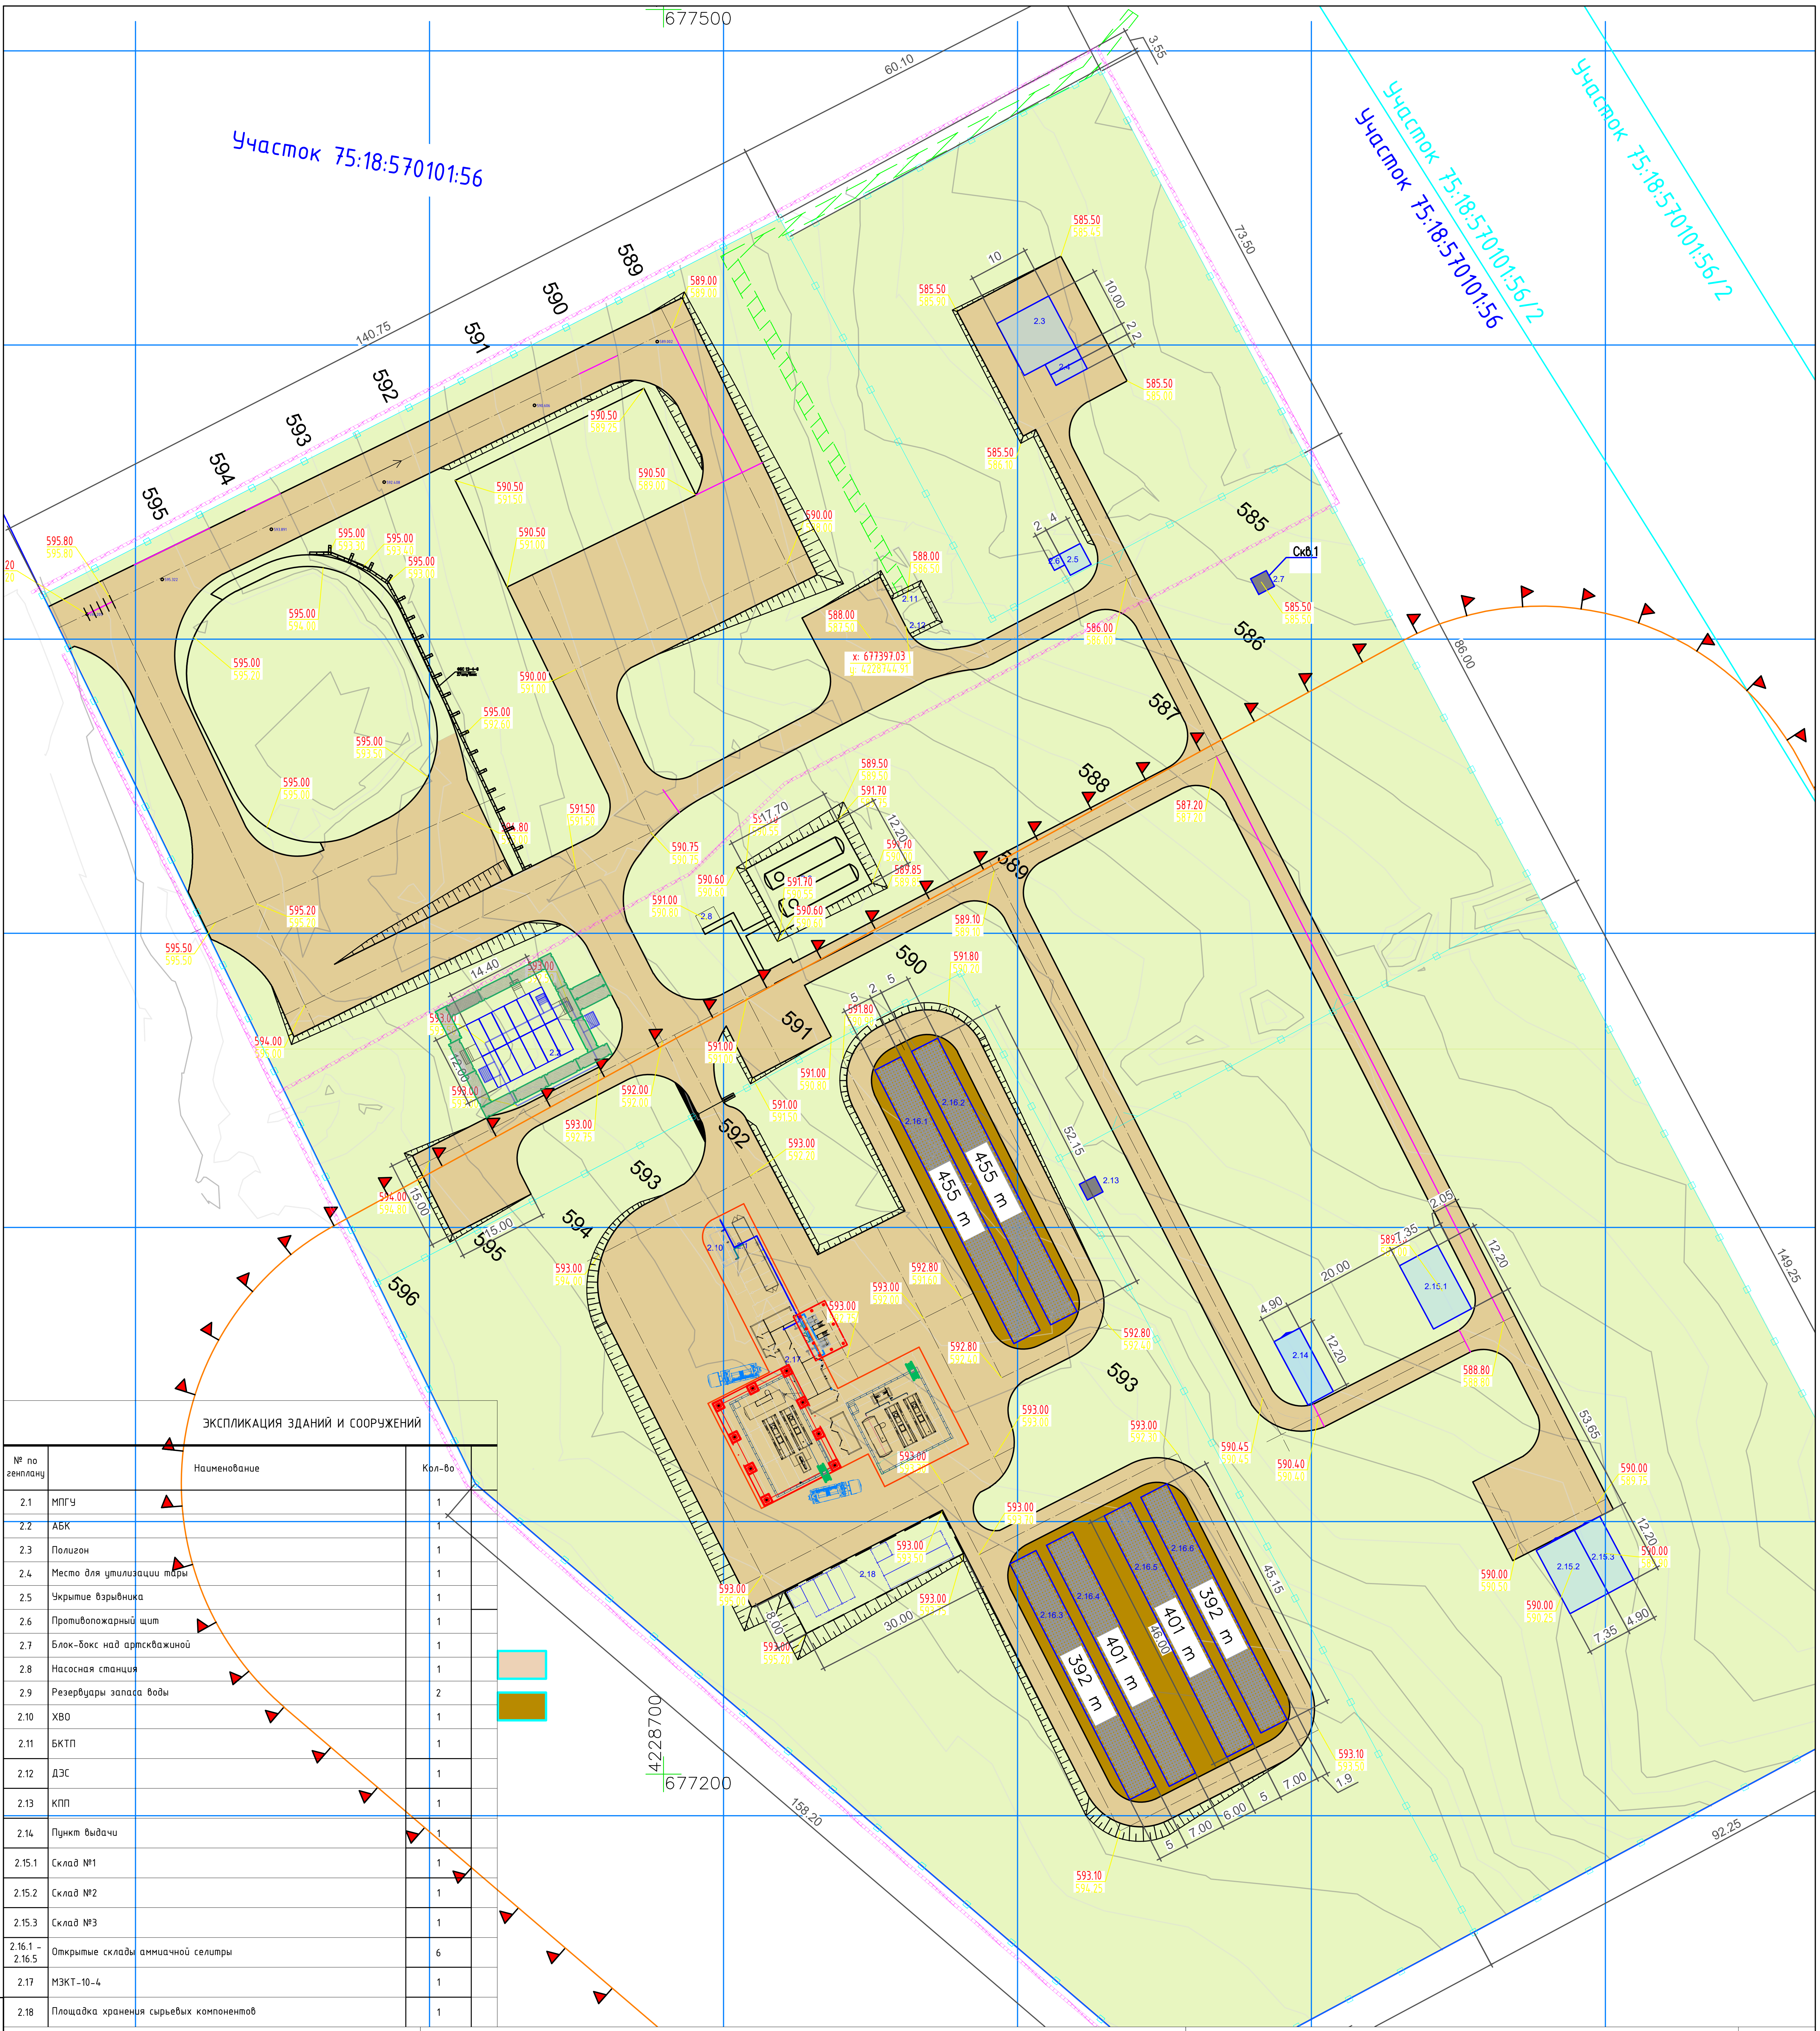

ЭКСПЛИКАЦИЯ ЗДАНИЙ И СООРУЖЕНИЙ

№ по генплану	Наименование	Кол-во
2.1	МПГУ	1
2.2	АБК	1
2.3	Полигон	1
2.4	Место для утилизации тары	1
2.5	Укрытие взрывника	1
2.6	Противопожарный щит	1
2.7	Блок-бокс над артскважиной	1
2.8	Насосная станция	1
2.9	Резервуары запаса воды	2
2.10	ХВО	1
2.11	БКТП	1
2.12	ДЭС	1
2.13	КПП	1
2.14	Пункт выдачи	1
2.15.1	Склад №1	1
2.15.2	Склад №2	1
2.15.3	Склад №3	1
2.16.1 – 2.16.5	Открытые склады аммиачной селитры	6
2.17	МЗКТ-10-4	1
2.18	Площадка хранения сырьевых компонентов	1

Сечение проезда, тип I

ПГС ГОСТ 23735-2014 - 250 мм
Георешетка GECARC Неосинт 0614
Геотекстиль GETPF Неосинт XU2185
ПГС ГОСТ 23735-2014 - 130 мм
Уплотнённый грунт земляного полотна

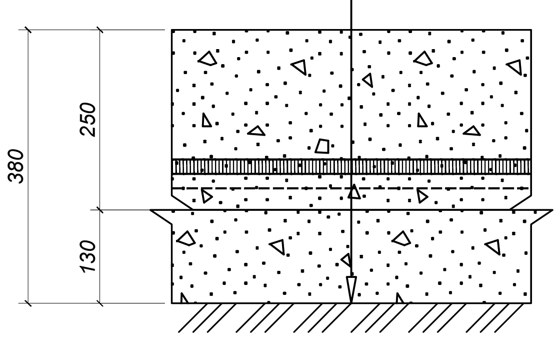

Сечение щебеночной канавы, тип III
(1:20)

Укрепление щебнем М600 фр.40-70 по ГОСТ 8267-93*
Геотекстиль GETPF Неосинт XU2185
Уплотнённый грунт земляного полотна

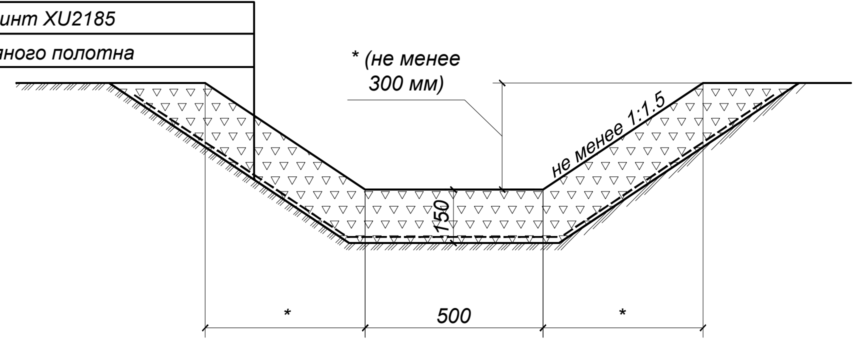

* размер уточнить по месту

Плита дорожная ПАГ-14
ПГС ГОСТ 23735-2014 – 0.32 м
Нетканный геотекстиль
Уплотнённый грунт

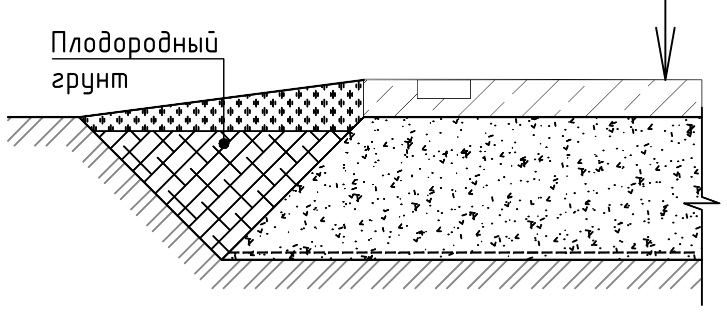

Условные обозначения

- ▶ ▶ ▶ Запретная зона (охранная)
- ▭ Автомобильные дороги (тип I)
- ▬ Площадки (тип III)

- Прочностные расчеты дорожной одежды выполнен согласно ГОСТР 71244–2024. Дороги автомобильные с низкой интенсивностью движения. Дорожная одежда. Конструирование и расчёт, в программном комплексе IndorPavement v26.3.0 компанией ООО "ГеоСМ".
- В местах пересечения автомобильных проездов с водопропускными канавами предусмотреть водопропускные трубы. Выпуск трубы за границы дорожного полотна не менее 2 м.

Изм.	Кол. уч.	Лист	# док.	Подп.	Дата
Разраб.		Дернов			10.26
Проверил		Гаскаров			10.26
Н. контр.		Исхакова			10.26
ГИП		Кадрачев			10.26

НСЗ/02/08-25ПД-ПЗУ

Разработка документации на размещение опасных производственных объектов: Этап I: «Пункт производства невзрывчатых компонентов эмульсионных ВВ марки «Сибирит®». Этап II: «Склад взрывчатых материалов вместимостью 49,9 т», расположенных по адресу: РФ, Забайкальский край, МР «Сретенский район», земельный участок с кадастровым номером 75:18:570101:208.

Схема планировочной организации земельного участка

Стадия	Лист	Листов
П	2	

Разбивочный план

ООО "ТЭК Инжиниринг"